



CONCEPT, NOT FOR FABRICATION


REV	DESCRIPTION	DATE	BY
P1	Concept sheet	2026-09-25	AC

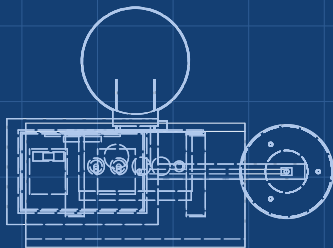


TOP VIEW
Scale 1:10

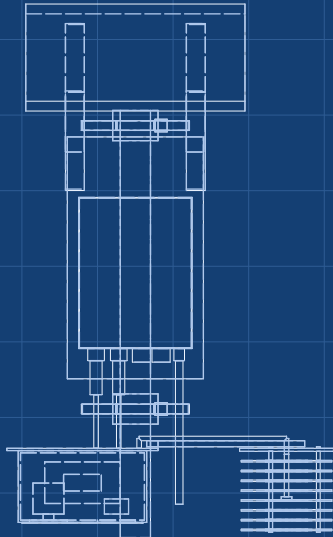

FRONT VIEW
Scale 1:10

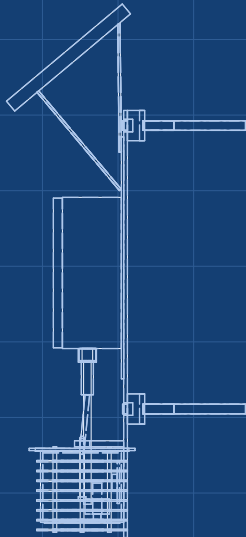

RIGHT VIEW
Scale 1:10

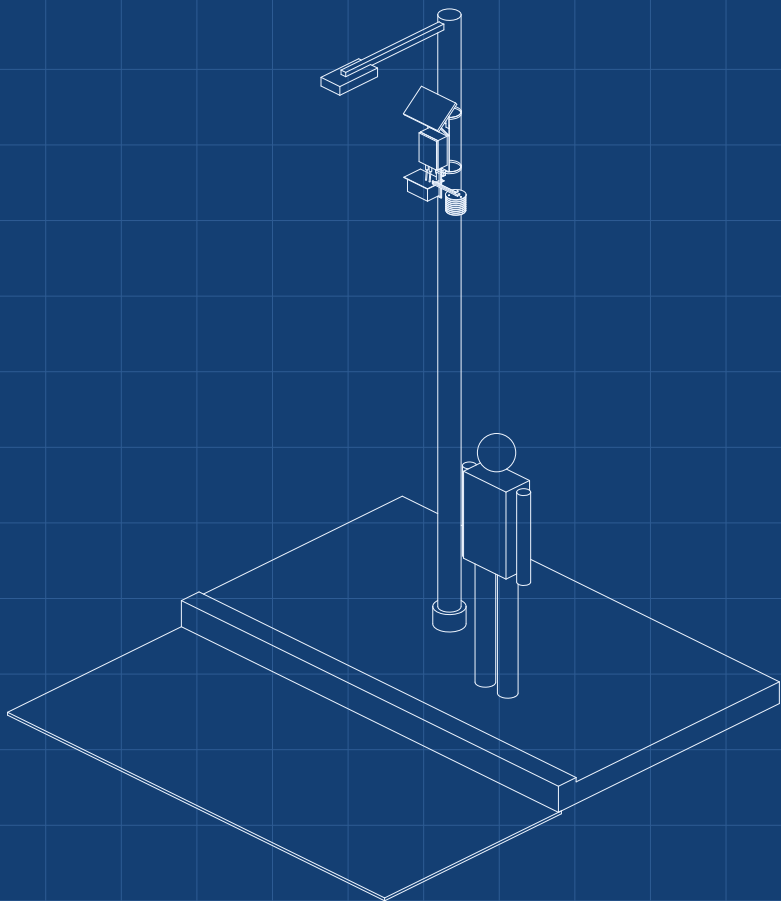

ISOMETRIC VIEW
Not to scale; grey is for scale

KEY FIGURES

PM2.5 (SPS30) and NO2 (B43F class), shielded T and RH
Inlets 3.0 m above the sidewalk; poles 80 to 200 mm
PM, T, RH checked on CalRig; NO2 by field collocation
48 mW design sensor load; 5 min records (AST-CAL-001)
3.65 kg and 0.14 m² on the pole (R13 not met)
Sensor head \$283; \$409 with FieldNode core

AIRSTREET

Street air quality node concept

DRAWING NO.

AST-DWG-010

REV

P1

SHEET

1 of 1

SIZE

ANSI B

SCALE

1:10

UNITS

mm

PROJECTION



DATE

2026-09-25

DRAWN

Amish Chadha

MATERIAL / NOTES

Massing model for concept communication