



CONCEPT, NOT FOR FABRICATION


REV	DESCRIPTION	DATE	BY
P1	Concept sheet	2026-09-25	AC

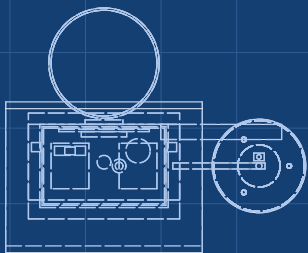


TOP VIEW
Scale 1:10

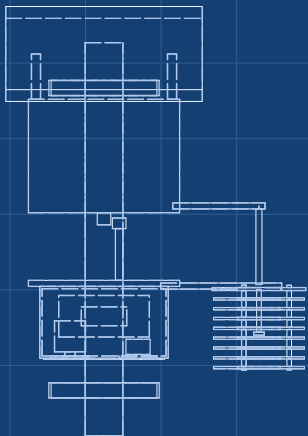

FRONT VIEW
Scale 1:10

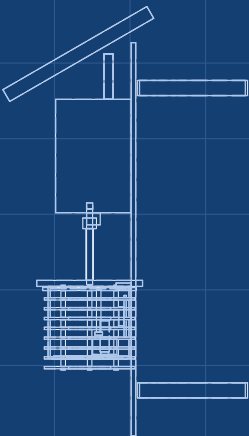

RIGHT VIEW
Scale 1:10

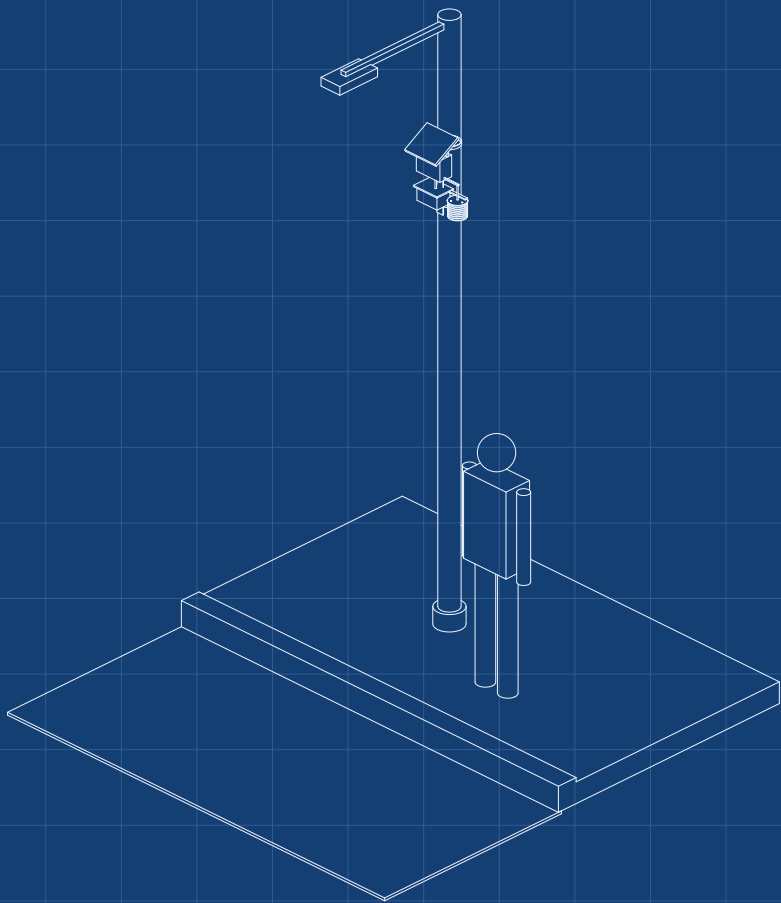

ISOMETRIC VIEW
Not to scale; grey is for scale

KEY FIGURES

PM2.5 (optical) and NO2 (electrochemical) with T and RH
Inlets about 3.0 m above the sidewalk (proposed)
PM, T, RH checked on CalRig; NO2 by field collocation
Sensors about 45 mW average; 5 min reports (estimate)
About 3.0 kg with FieldNode core (estimate)
About \$391 in parts with FieldNode core (indicative)

AIRSTREET

Street air quality node concept

DRAWING NO. AST-DWG-010		REV P1	SHEET 1 of 1	SIZE ANSI B
SCALE 1:10	UNITS mm	PROJECTION 	DATE 2026-09-25	DRAWN Amish Chadha

MATERIAL / NOTES
Massing model for concept communication