



CONCEPT, NOT FOR FABRICATION


REV	DESCRIPTION	DATE	BY
P1	Concept sheet	2026-09-25	AC

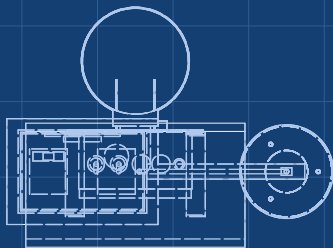


TOP VIEW
Scale 1:10

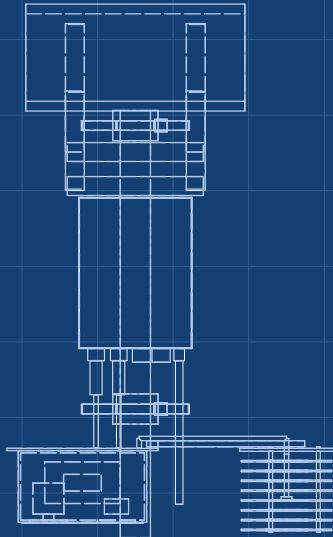

FRONT VIEW
Scale 1:10

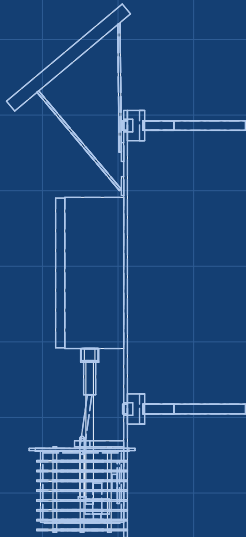

RIGHT VIEW
Scale 1:10

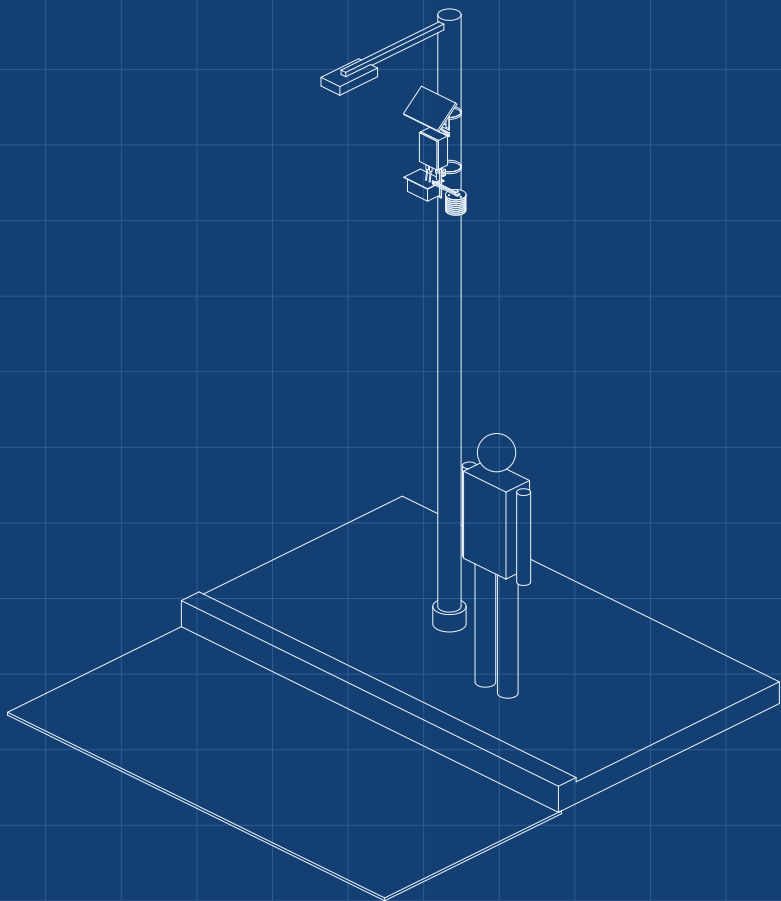

ISOMETRIC VIEW
Not to scale; grey is for scale

KEY FIGURES

PM2.5 (SPS30) and NO2 (B43F class), shielded T and RH
Inlets 3.0 m above the sidewalk; poles 80 to 200 mm
PM, T, RH checked on CalRig; NO2 by field collocation
87 mW design sensor load; 5 min records (15 min on TTN)
3.26 kg and 0.126 m² on the pole (FieldNode back plate left off)
Sensor head \$285; \$411 with FieldNode core

AIRSTREET

Street air quality node concept

DRAWING NO. AST-DWG-010		REV P1	SHEET 1 of 1	SIZE ANSI B
SCALE 1:10	UNITS mm	PROJECTION 	DATE 2026-09-25	DRAWN Amish Chadha

MATERIAL / NOTES
Massing model for concept communication