


CONCEPT, NOT FOR FABRICATION


AirStreet · github.com/BoujeeEnjinia1701/airstreet

REV	DESCRIPTION	DATE	BY
P1	Concept sheet	2026-10-02	AC

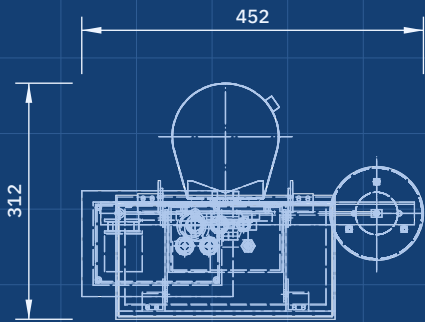


TOP VIEW

Scale 1:10; looking down (along -Z)

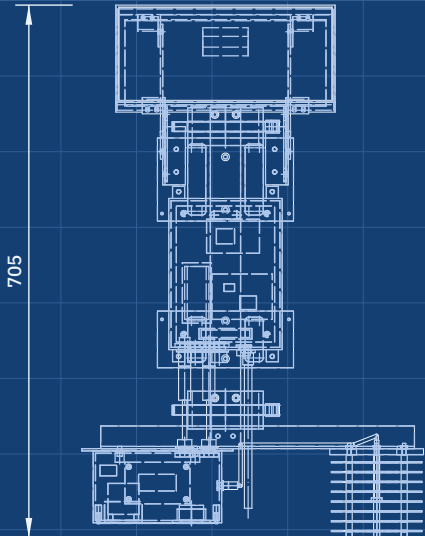


FRONT VIEW

Scale 1:10; looking at the front (along +Y)

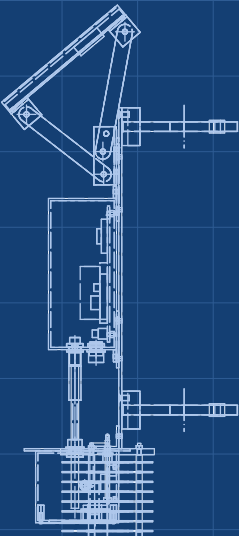

RIGHT VIEW

Scale 1:10; looking at the right side (along -X)

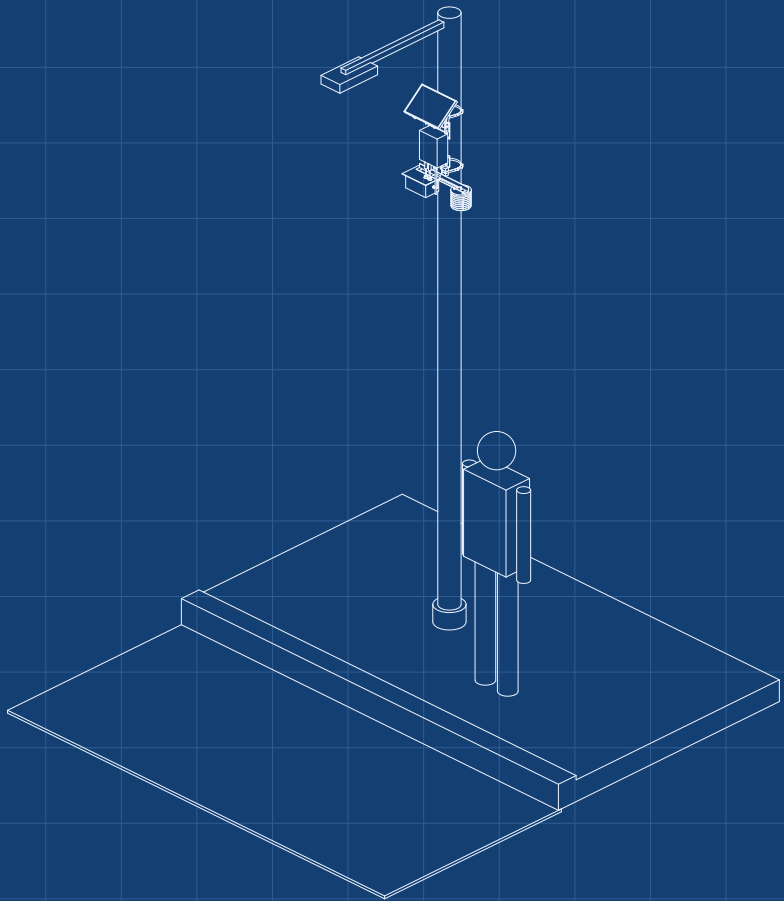

ISOMETRIC VIEW

Not to scale; grey is for scale; seen from the front right and above, about 30 deg elevation

KEY FIGURES

PM2.5 (SPS30) and NO2 (B43F class), shielded T and RH
Inlets 3.0 m above the sidewalk; poles 80 to 200 mm
PM, T, RH checked on CalRig; NO2 by field collocation
87 mW design sensor load; 5 min records (15 min on TTN)
3.62 kg (3.78 kg with sun shield) and 0.139 m² on the pole
Sensor head \$302.50; \$433.50 with FieldNode core

AIRSTREET

github.com/BoujeeEnjinia1701/airstreet

Street air quality node concept

DRAWING NO. AST-DWG-010			REV P1	SHEET 1 of 1	SIZE ANSI B
SCALE 1:10	UNITS mm	PROJECTION 	DATE 2026-10-02	DRAWN Amish Chadha	

MATERIAL / NOTES
Massing model for concept communication