
CONCEPT, NOT FOR FABRICATION


AirStreet · github.com/BoujeeEnjinia1701/airstreet

REV	DESCRIPTION	DATE	BY
P1	Concept sheet	2026-10-24	AC

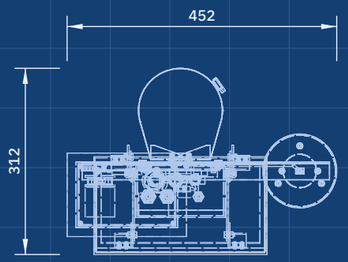


TOP VIEW

Scale 1:10; looking down (along -Z)

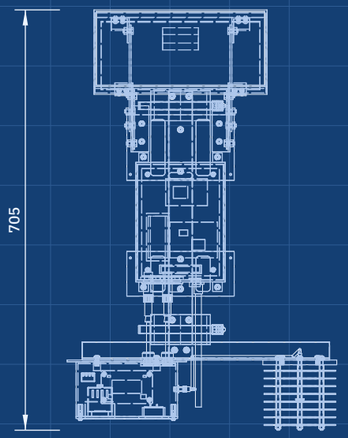


FRONT VIEW

Scale 1:10; looking at the front (along +Y)

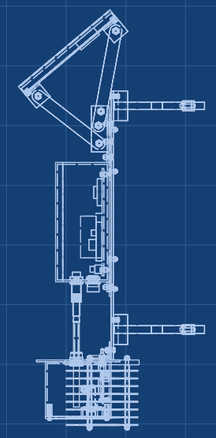

RIGHT VIEW

Scale 1:10; looking at the right side (along -X)

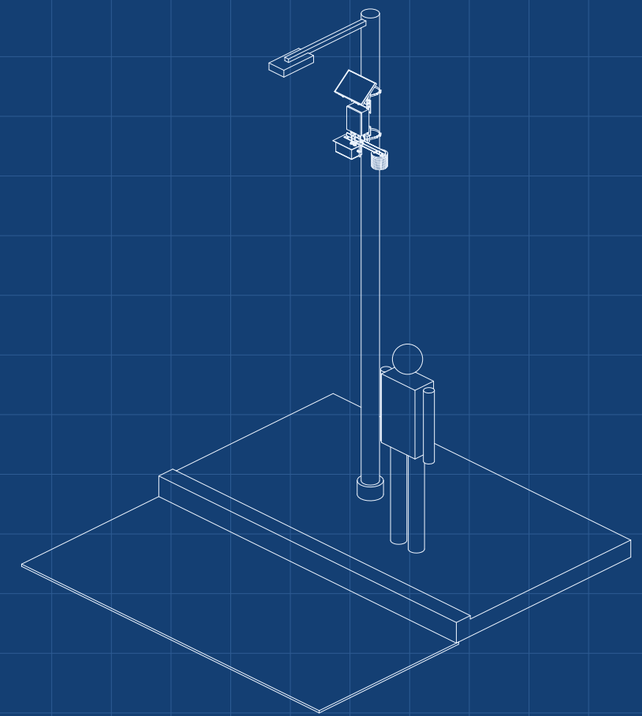

ISOMETRIC VIEW

Not to scale; grey is for scale; seen from the front right and above, about 30 deg elevation

KEY FIGURES

- PM2.5 (SPS30) and NO2 (B43F class), shielded T and RH
- Inlets 3.0 m above the sidewalk; poles 80 to 200 mm
- PM, T, RH checked on CalRig; NO2 by field collocation
- 87 mW design sensor load; 5 min records (15 min on TTN)
- 3.61 kg (3.77 kg with sun shield) and 0.139 m² on the pole
- Sensor head $302.50; $433.50 with FieldNode core

AIRSTREET

github.com/BoujeeEnjinia1701/airstreet

Street air quality node concept

DRAWING NO.	REV	SHEET	SIZE
AST-DWG-010	P1	1 of 1	ANSI B

SCALE	UNITS	PROJECTION	DATE	DRAWN
1:10	mm		2026-10-24	Amish Chadha

MATERIAL / NOTES

Massing model for concept communication

Licensed CERN-OHL-S-2.0 · Design Molecule Lab · designmolecule.com

Generated from cad/src; do not edit by hand